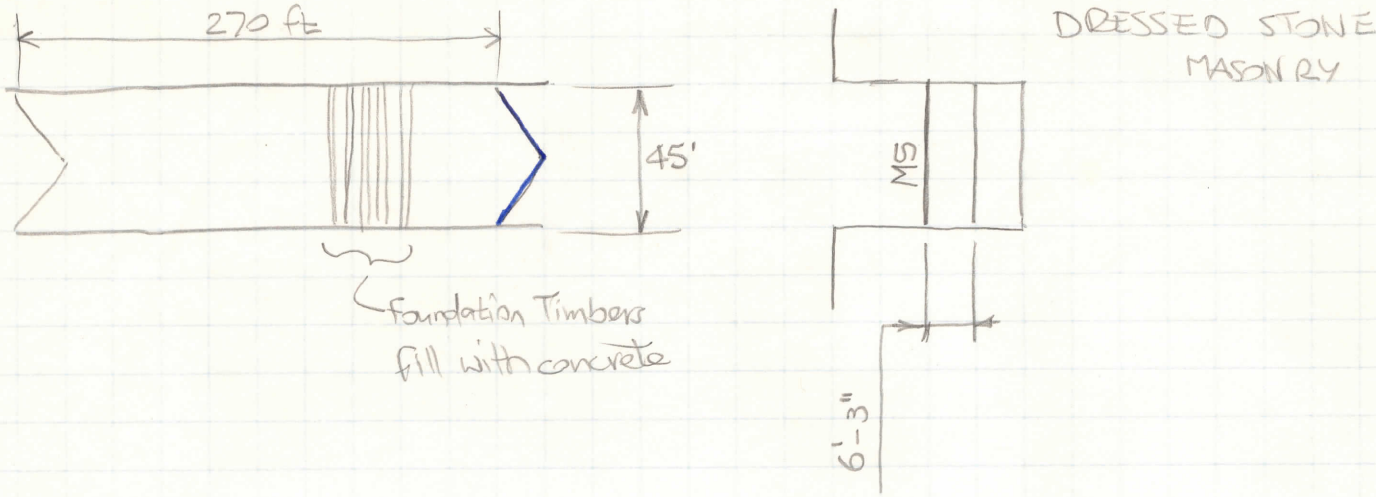
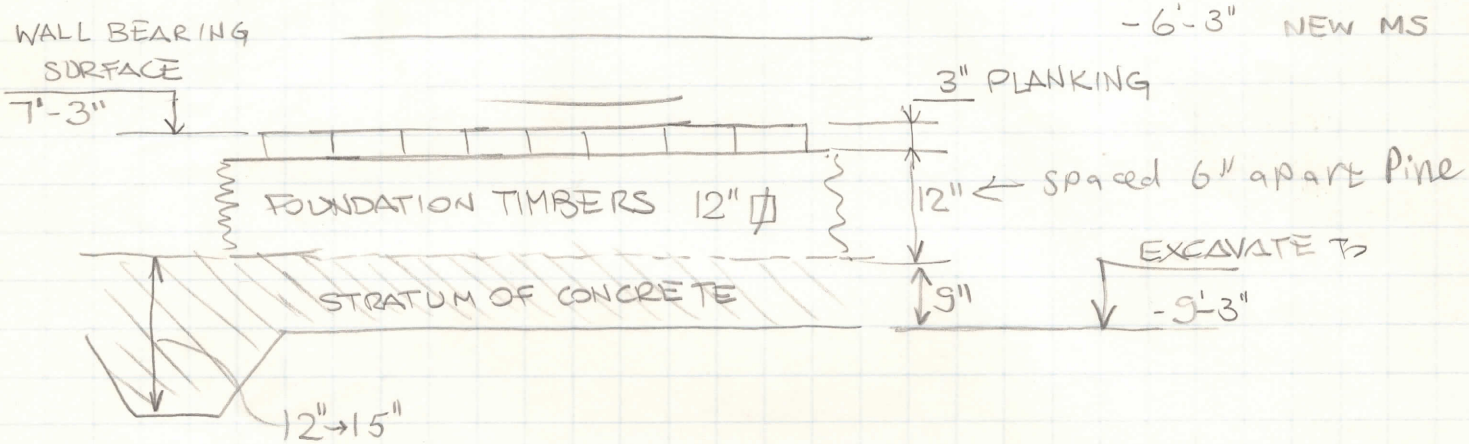
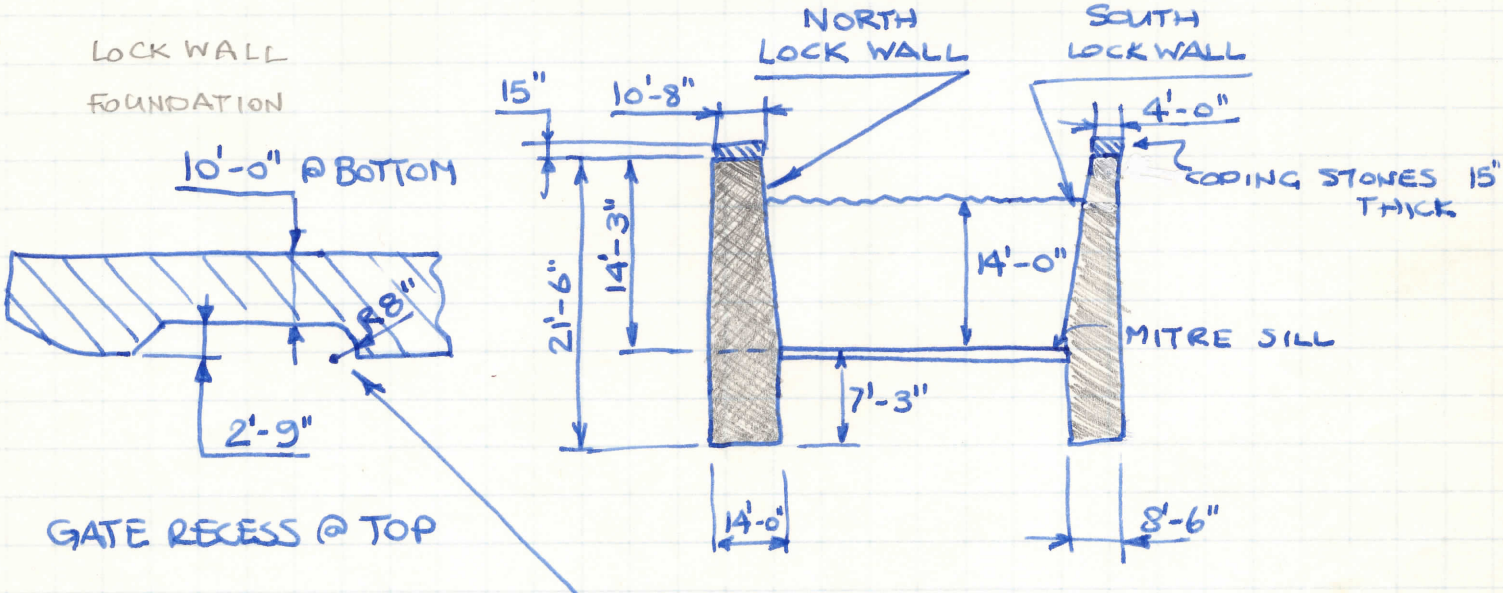

270 ft
45'
Foundation Timbers
fill with concrete
DRESSED STONE
MASONRY
MS
6'-3"


WALL BEARING
SURFACE
7'-3"
-6'-3" NEW MS
3" PLANKING
FOUNDATION TIMBERS 12" □
12" ← spaced 6" apart Pine
EXCAVATE TO
-9'-3"
STRATUM OF CONCRETE
9"
12"→15"


LOCK WALL
FOUNDATION
10'-0" @ BOTTOM
8"
2'-9"
GATE RECESS @ TOP
NORTH
LOCK WALL
SOUTH
LOCK WALL
15"
10'-8"
4'-0"
COPING STONES 15"
THICK
21'-6"
14'-3"
14'-0"
MITRE SILL
7'-3"
14'-0"
8'-6"
HOLLOW QUOIN