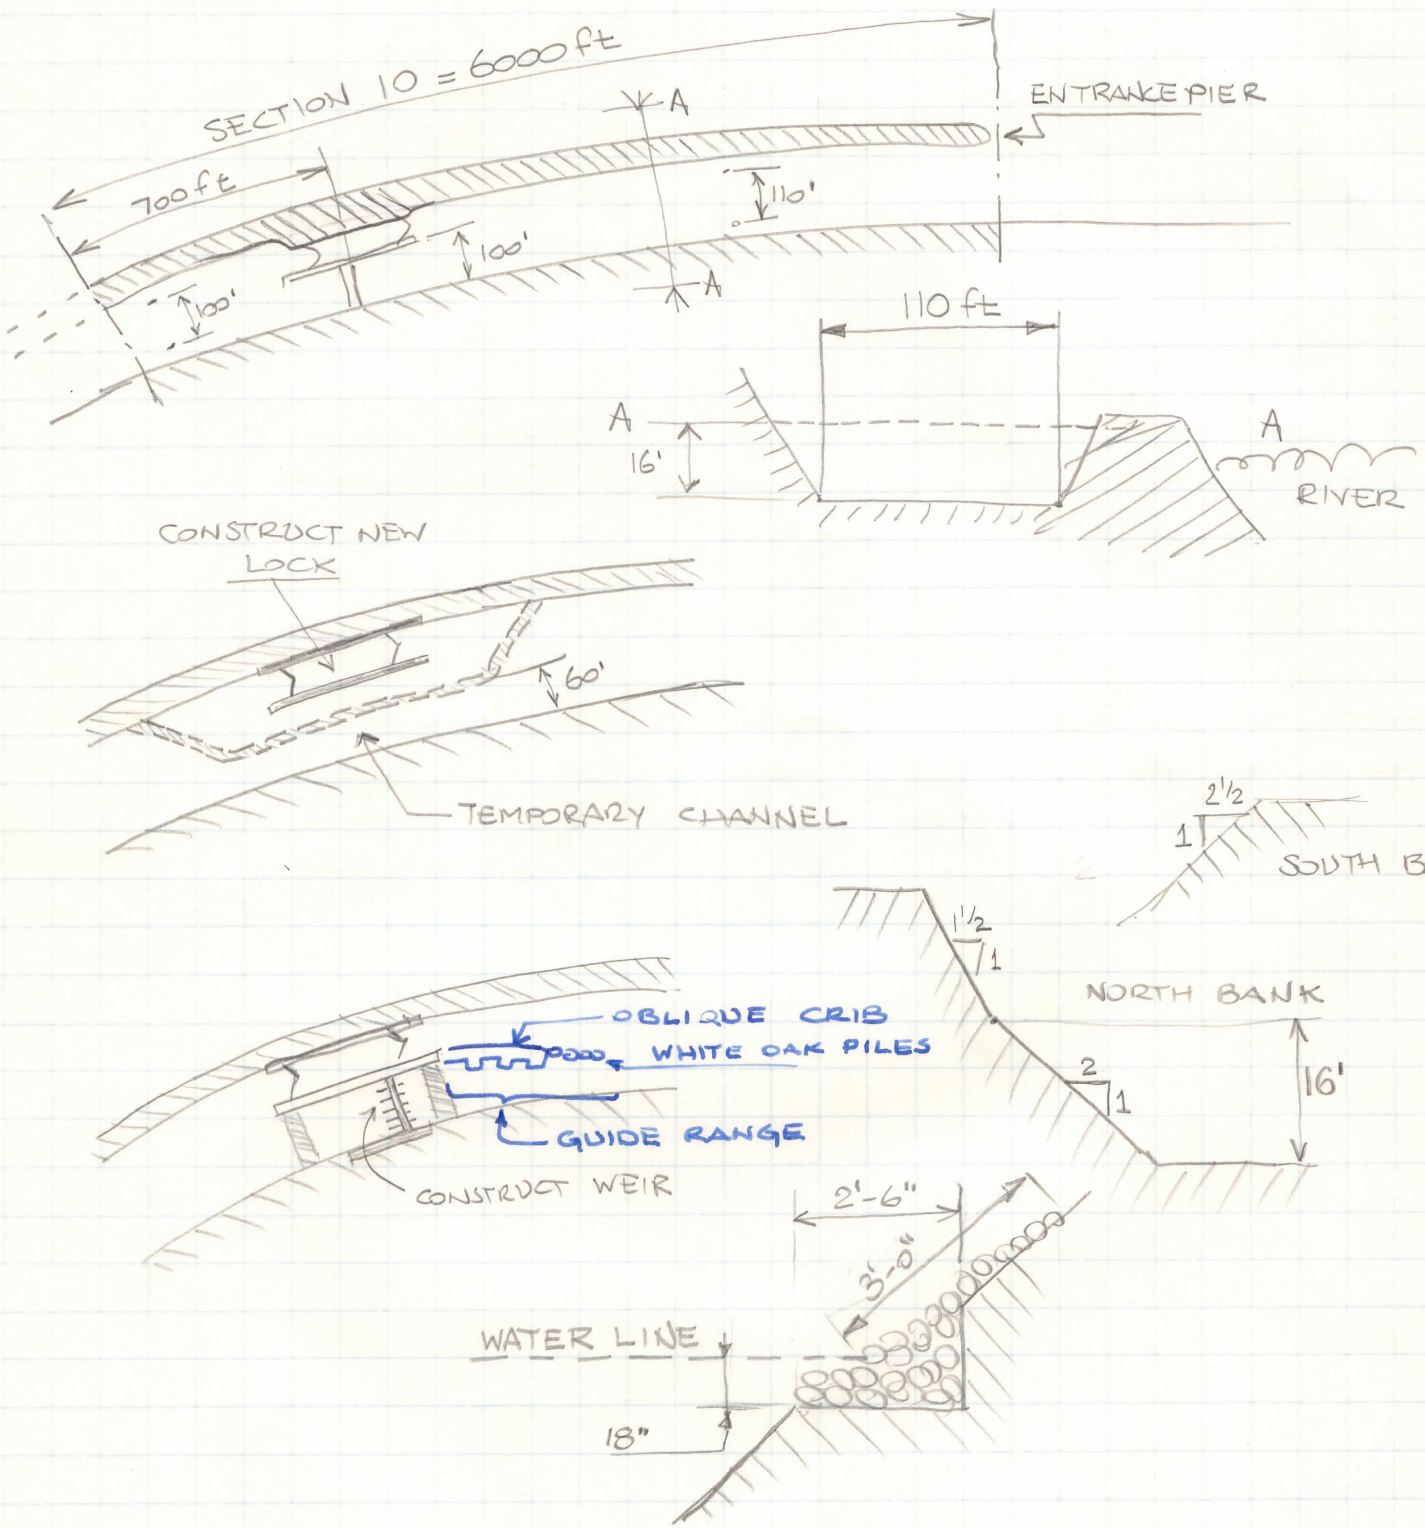

SECTION 10 = 6000 ft
700 ft
100'
100'
A
A
110'
ENTRANCE PIER
110 ft
A
16'
A
RIVER
CONSTRUCT NEW LOCK
60'
TEMPORARY CHANNEL
2½
1
SOUTH BANK
1½
1
NORTH BANK
16'
2
1
OBLIQUE CRIB
WHITE OAK PILES
GUIDE RANGE
CONSTRUCT WEIR
2'-6"
3'-0"
WATER LINE
18"