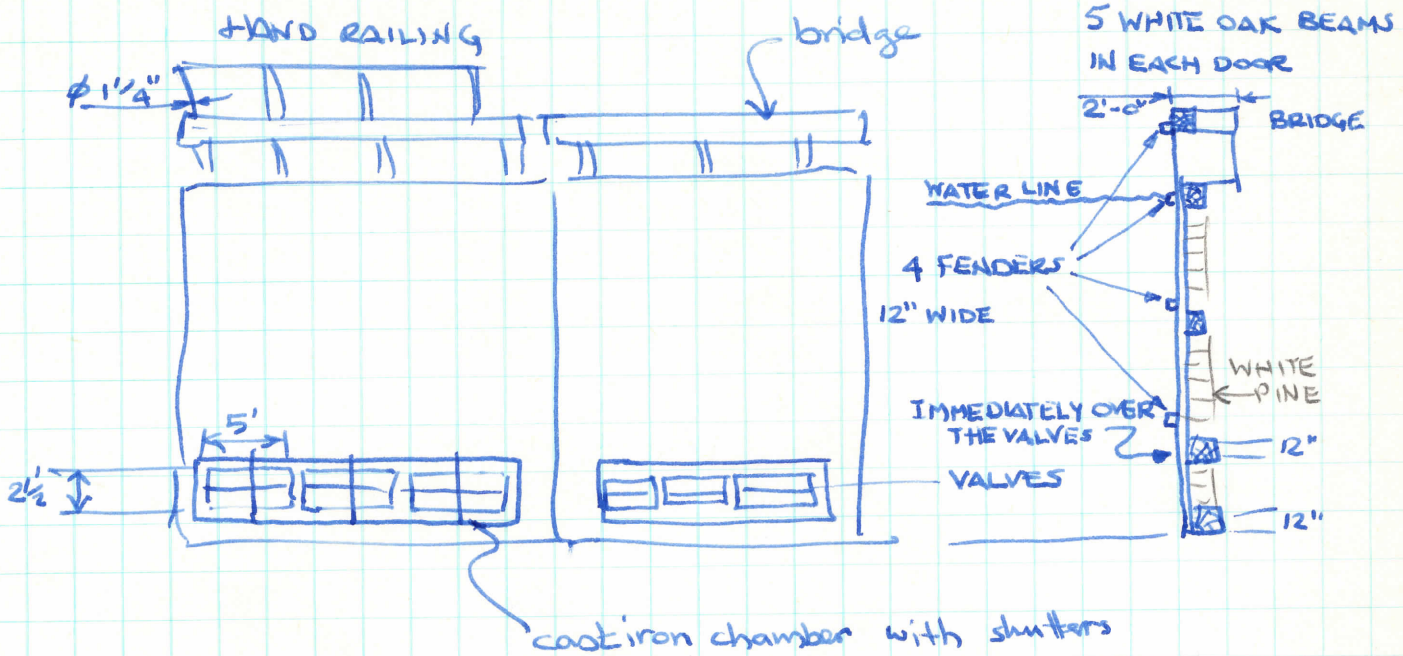
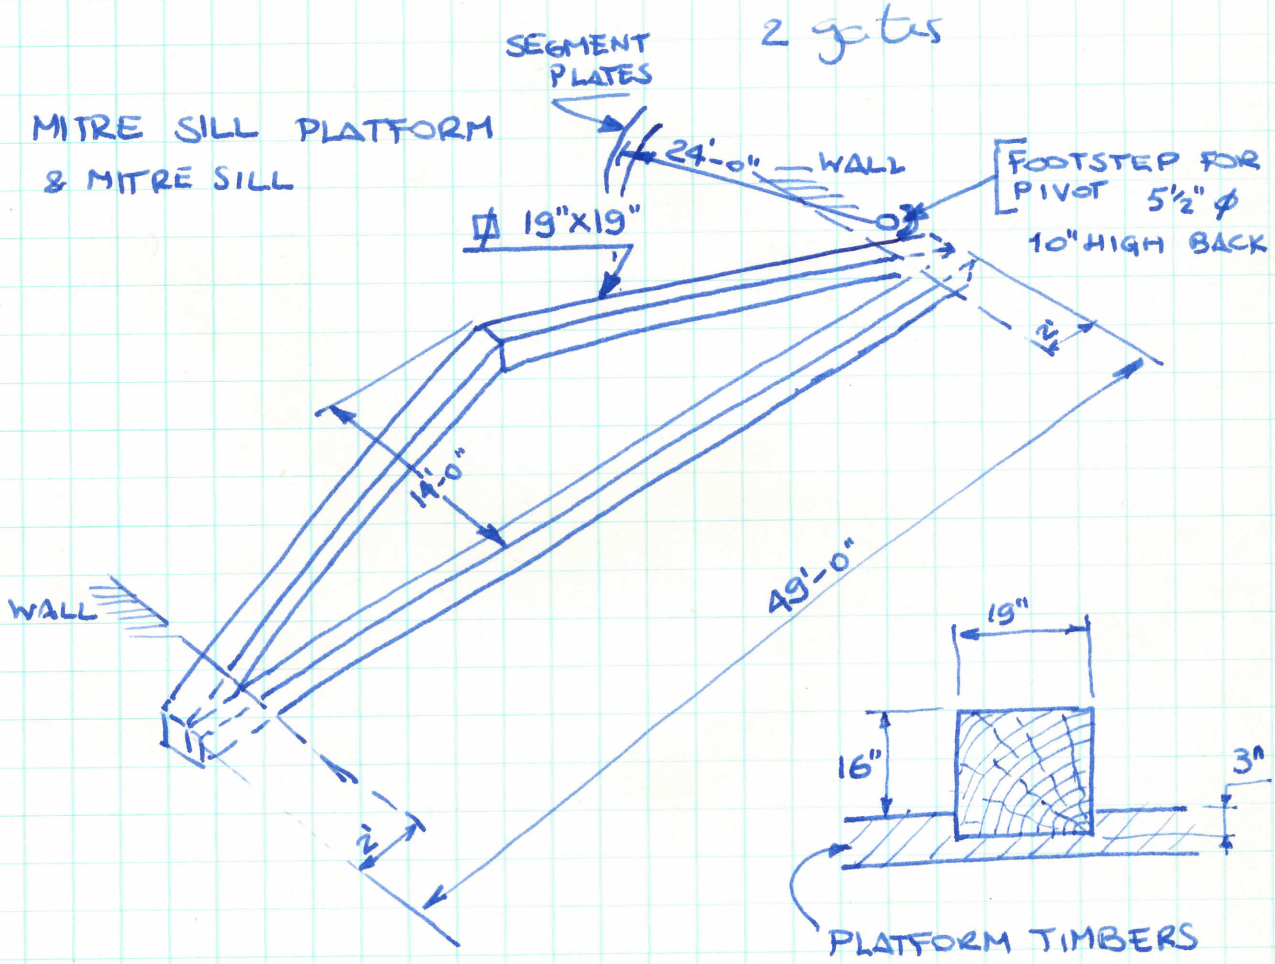

HAND RAILING
bridge
5 WHITE OAK BEAMS IN EACH DOOR
2'-0"
BRIDGE
WATER LINE
4 FENDERS
12" WIDE
WHITE PINE
IMMEDIATELY OVER THE VALVES
12"
VALVES
12"
5'
2½'
cast iron chamber with shutters

2 gates


SEGMENT PLATES
MITRE SILL PLATFORM & MITRE SILL
24'-0"
WALL
FOOTSTEP FOR PIVOT 5½" ϕ 10" HIGH BACK
19"x19"
2½'
14'-0"
49'-0"
WALL
2'
19"
16"
3"
PLATFORM TIMBERS